



1:1)

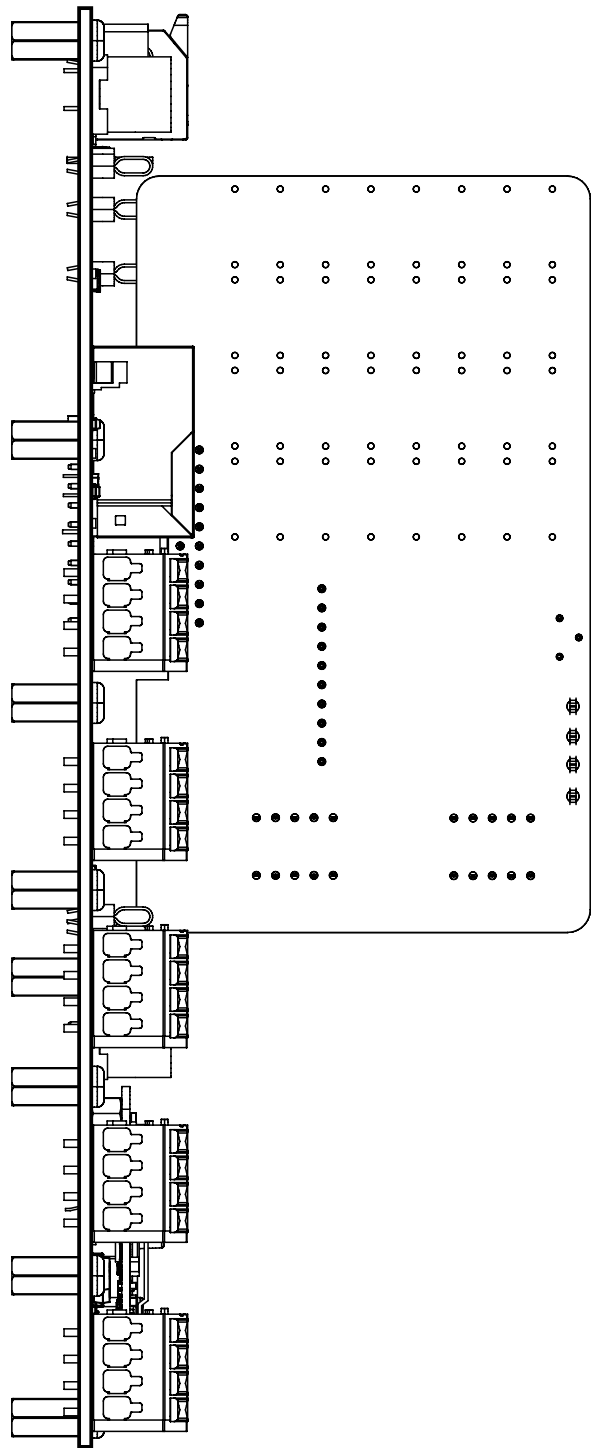


Top side (Scale 1:1)

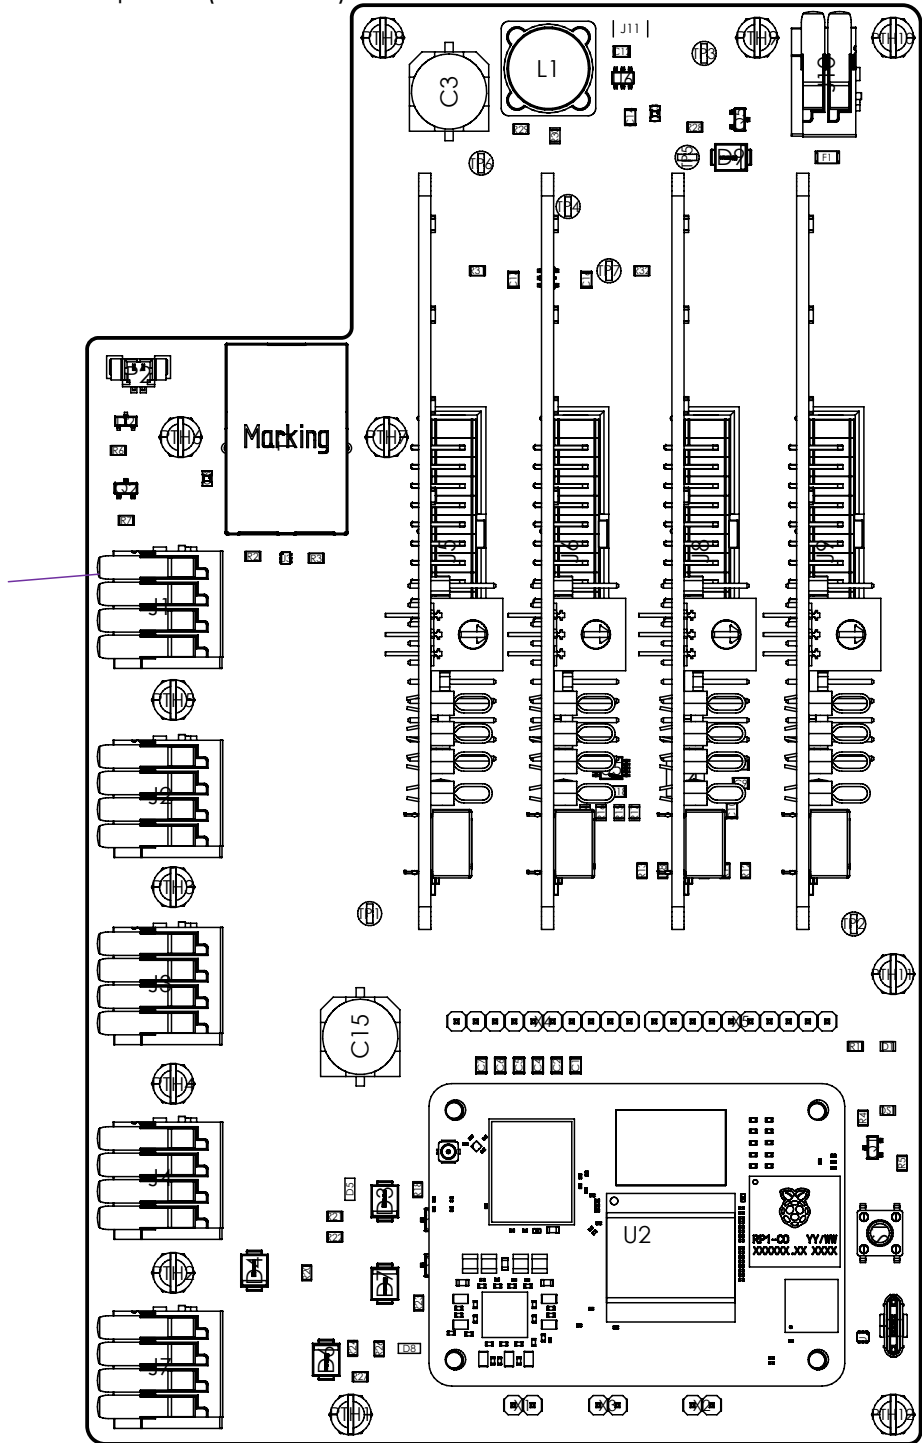

NOTES UNLESS OTHERWISE SPCEIFIED:


- 1. NOTE
- 2. NOTE
- 3. NOTE

Front side (Scale 1:1)

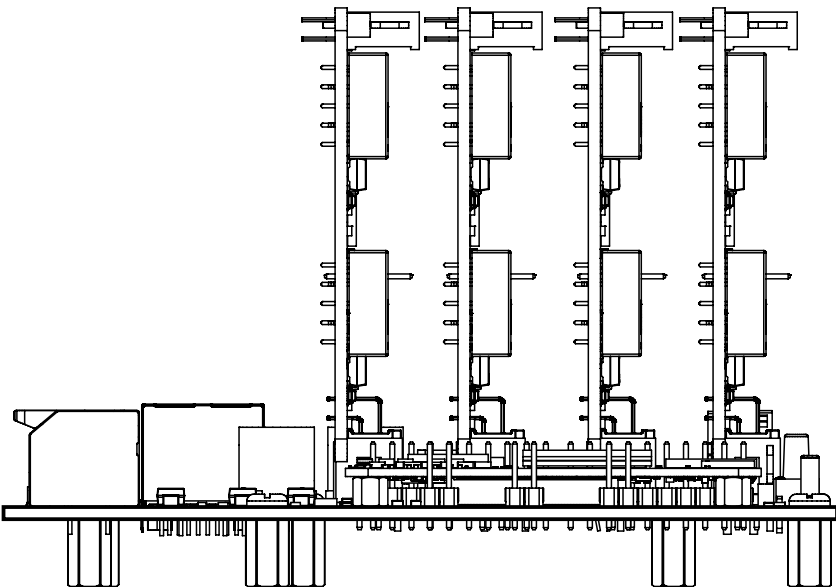


ETML Rue de Sébeillon 12 1004 Lausanne +41 316 77 77 www.etml.ch	Mod.	a	.	Dessiné	Léo Mendes	02.09.2025	A3		Echelle : 2:1
		b	.	Contrôlé	-	-			
		c	.				Nb. feuilles	Feuille n°	
		d	.	Remplace	.	=DRAFT	4	1	
	Nom du projet RegulationChauffage_Motherboard New						No 2510		


Bottom side (Scale 1:1)

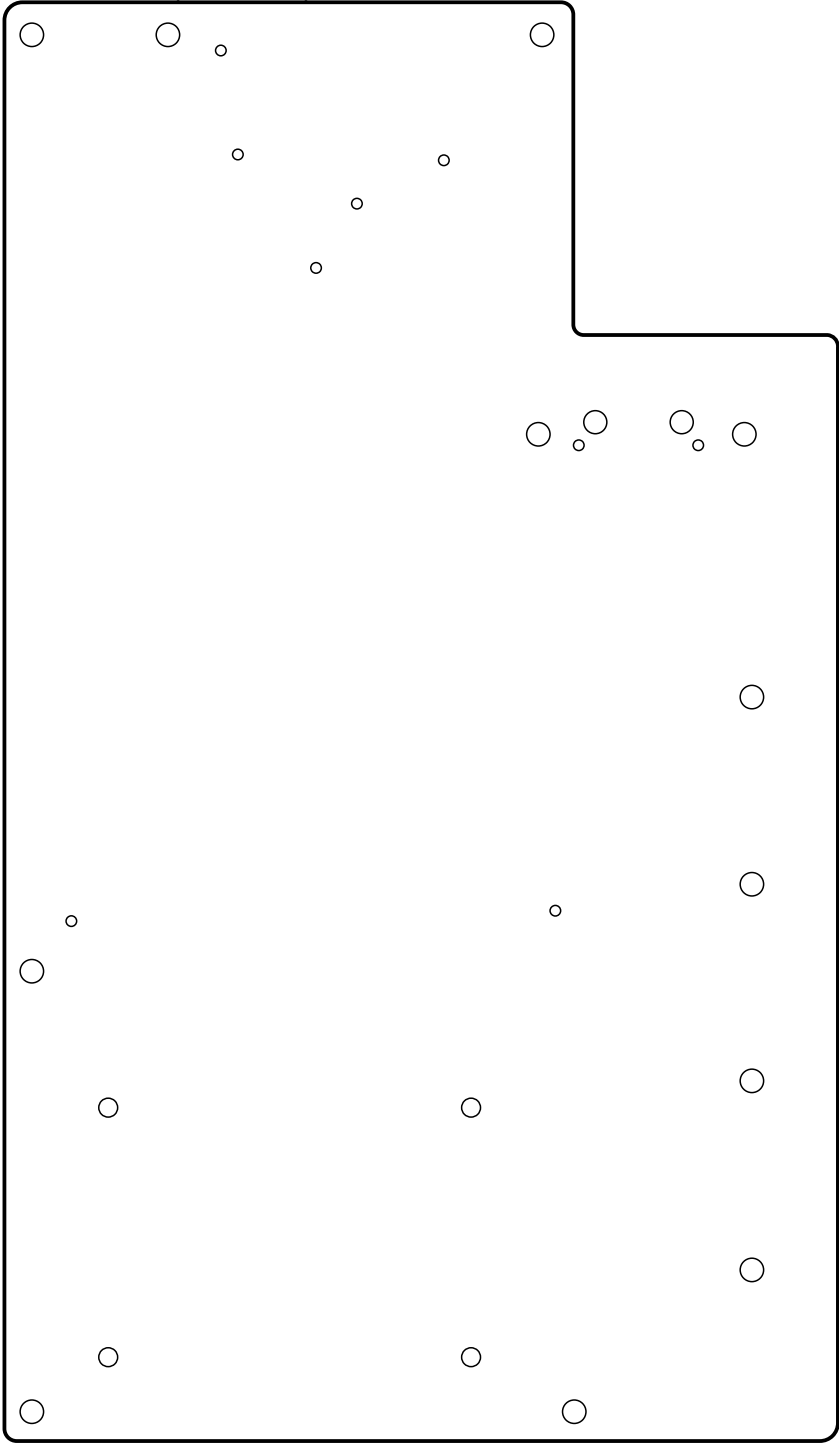

Back side (Scale 1:1)

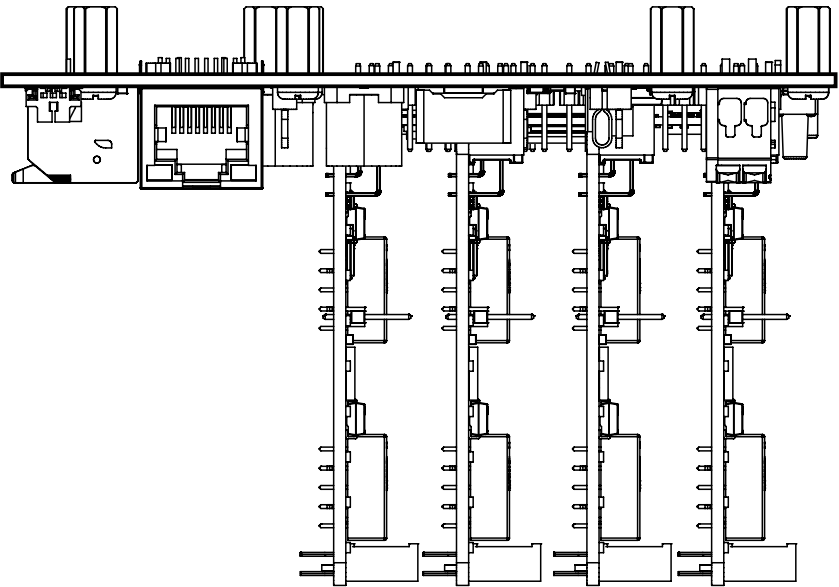


Right side (Scale 1:1)

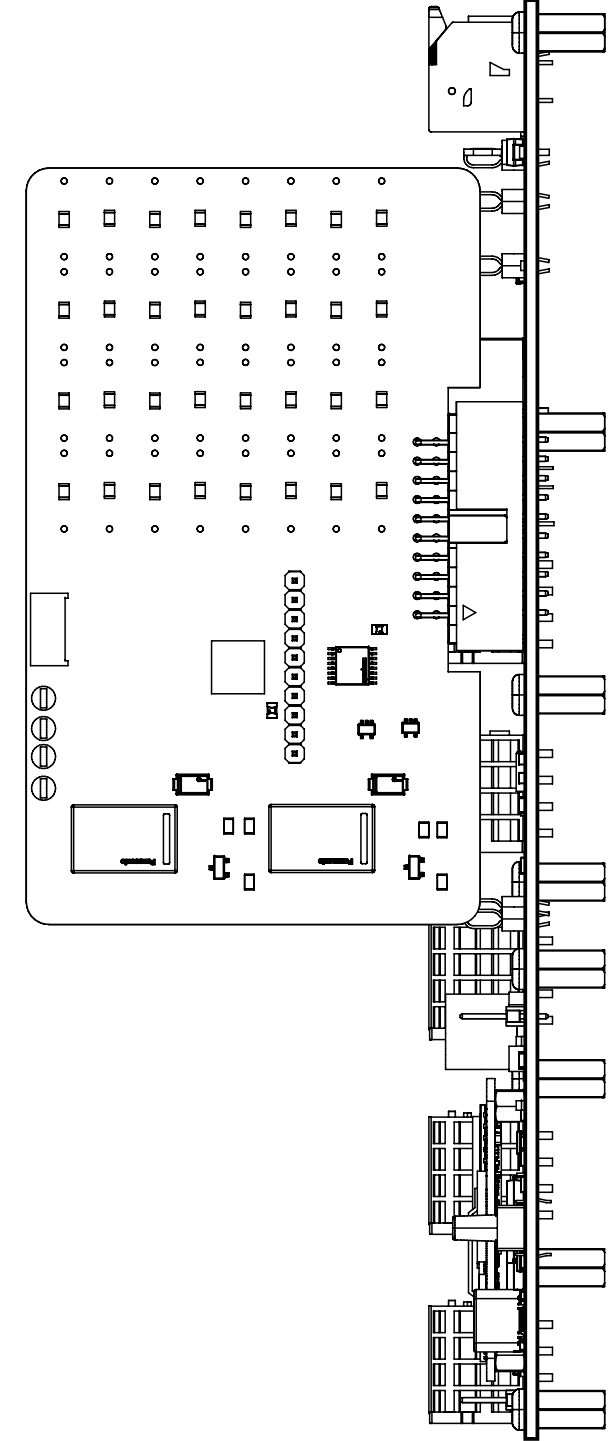


ETML Rue de Sébeillon 12 1004 Lausanne +41 316 77 77 www.etml.ch	Mod.	a	.	Dessiné	Léo Mendes	02.09.2025	A3		Echelle : 2:1
		b	.	Contrôlé	-	-			
		c	.				Nb. feuilles	Feuille n°	
		d	.	Remplace	.	=DRAFT	4	2	
	Nom du projet RegulationChauffage_Motherboard						No 2510		

Top Layer (Scale 1:1)

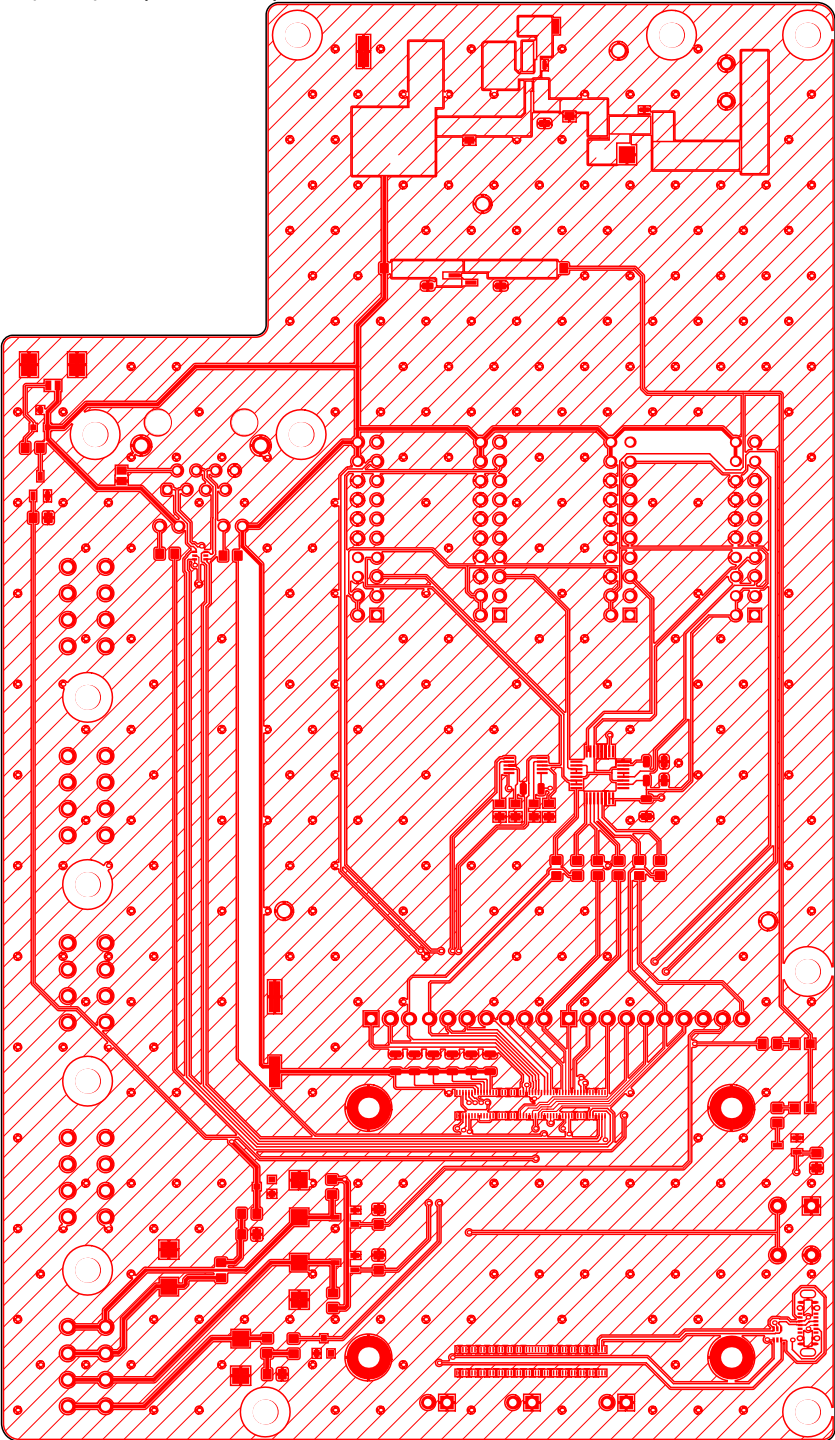

Bottom Layer (Scale 1:1)

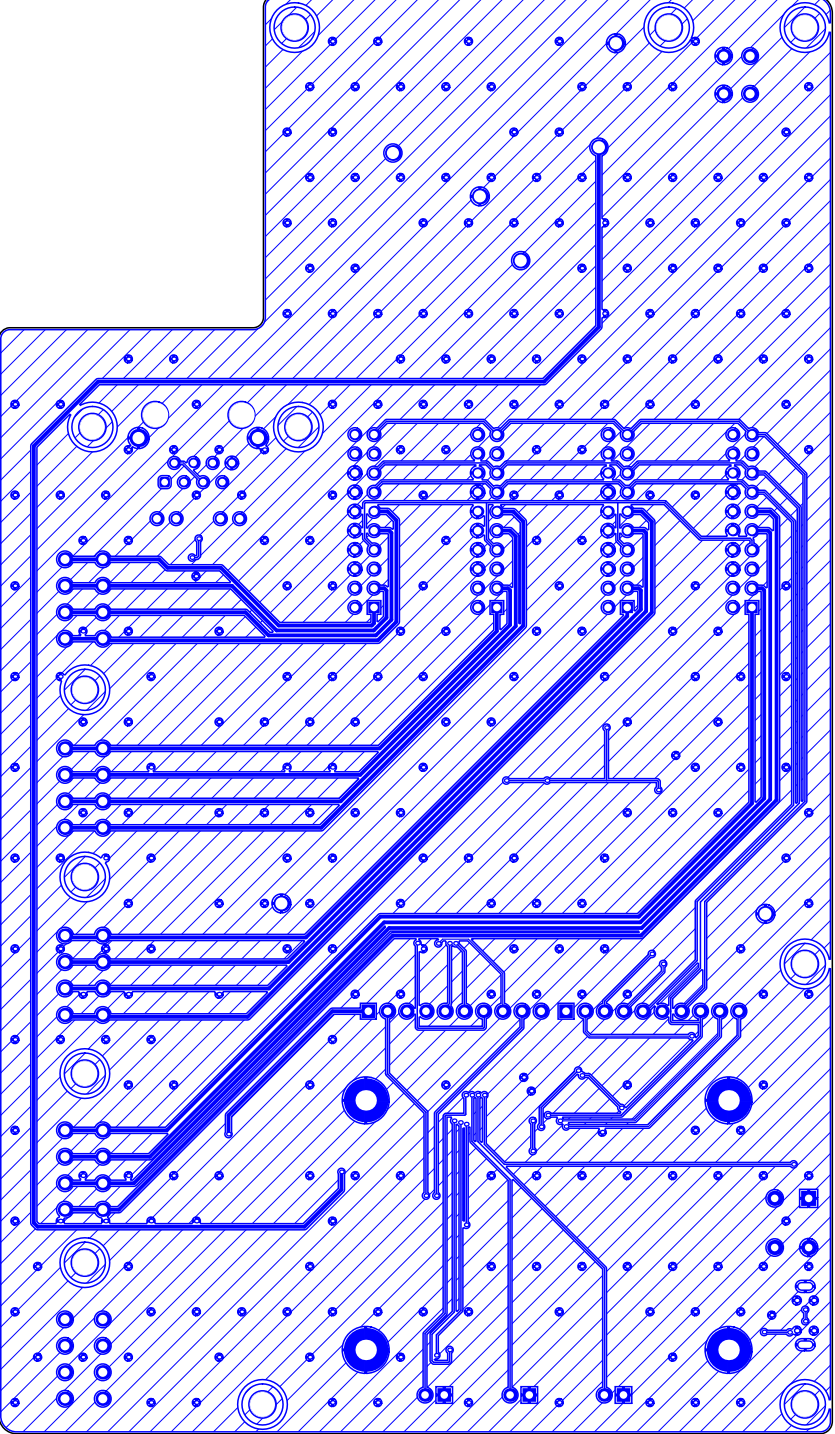

ETML Rue de Sébeillon 12 1004 Lausanne +41 316 77 77 www.etml.ch	Mod.	a	.	Dessiné	Léo Mendes	02.09.2025	A3		Echelle : 2:1
		b	.	Contrôlé	-	-			
		c	.				Nb. feuilles	Feuille n°	
		d	.	Remplace	.		4	3	
	Nom du projet RegulationChauffage_Motherboard						No 2510		


4

3

2

1

Realistic View

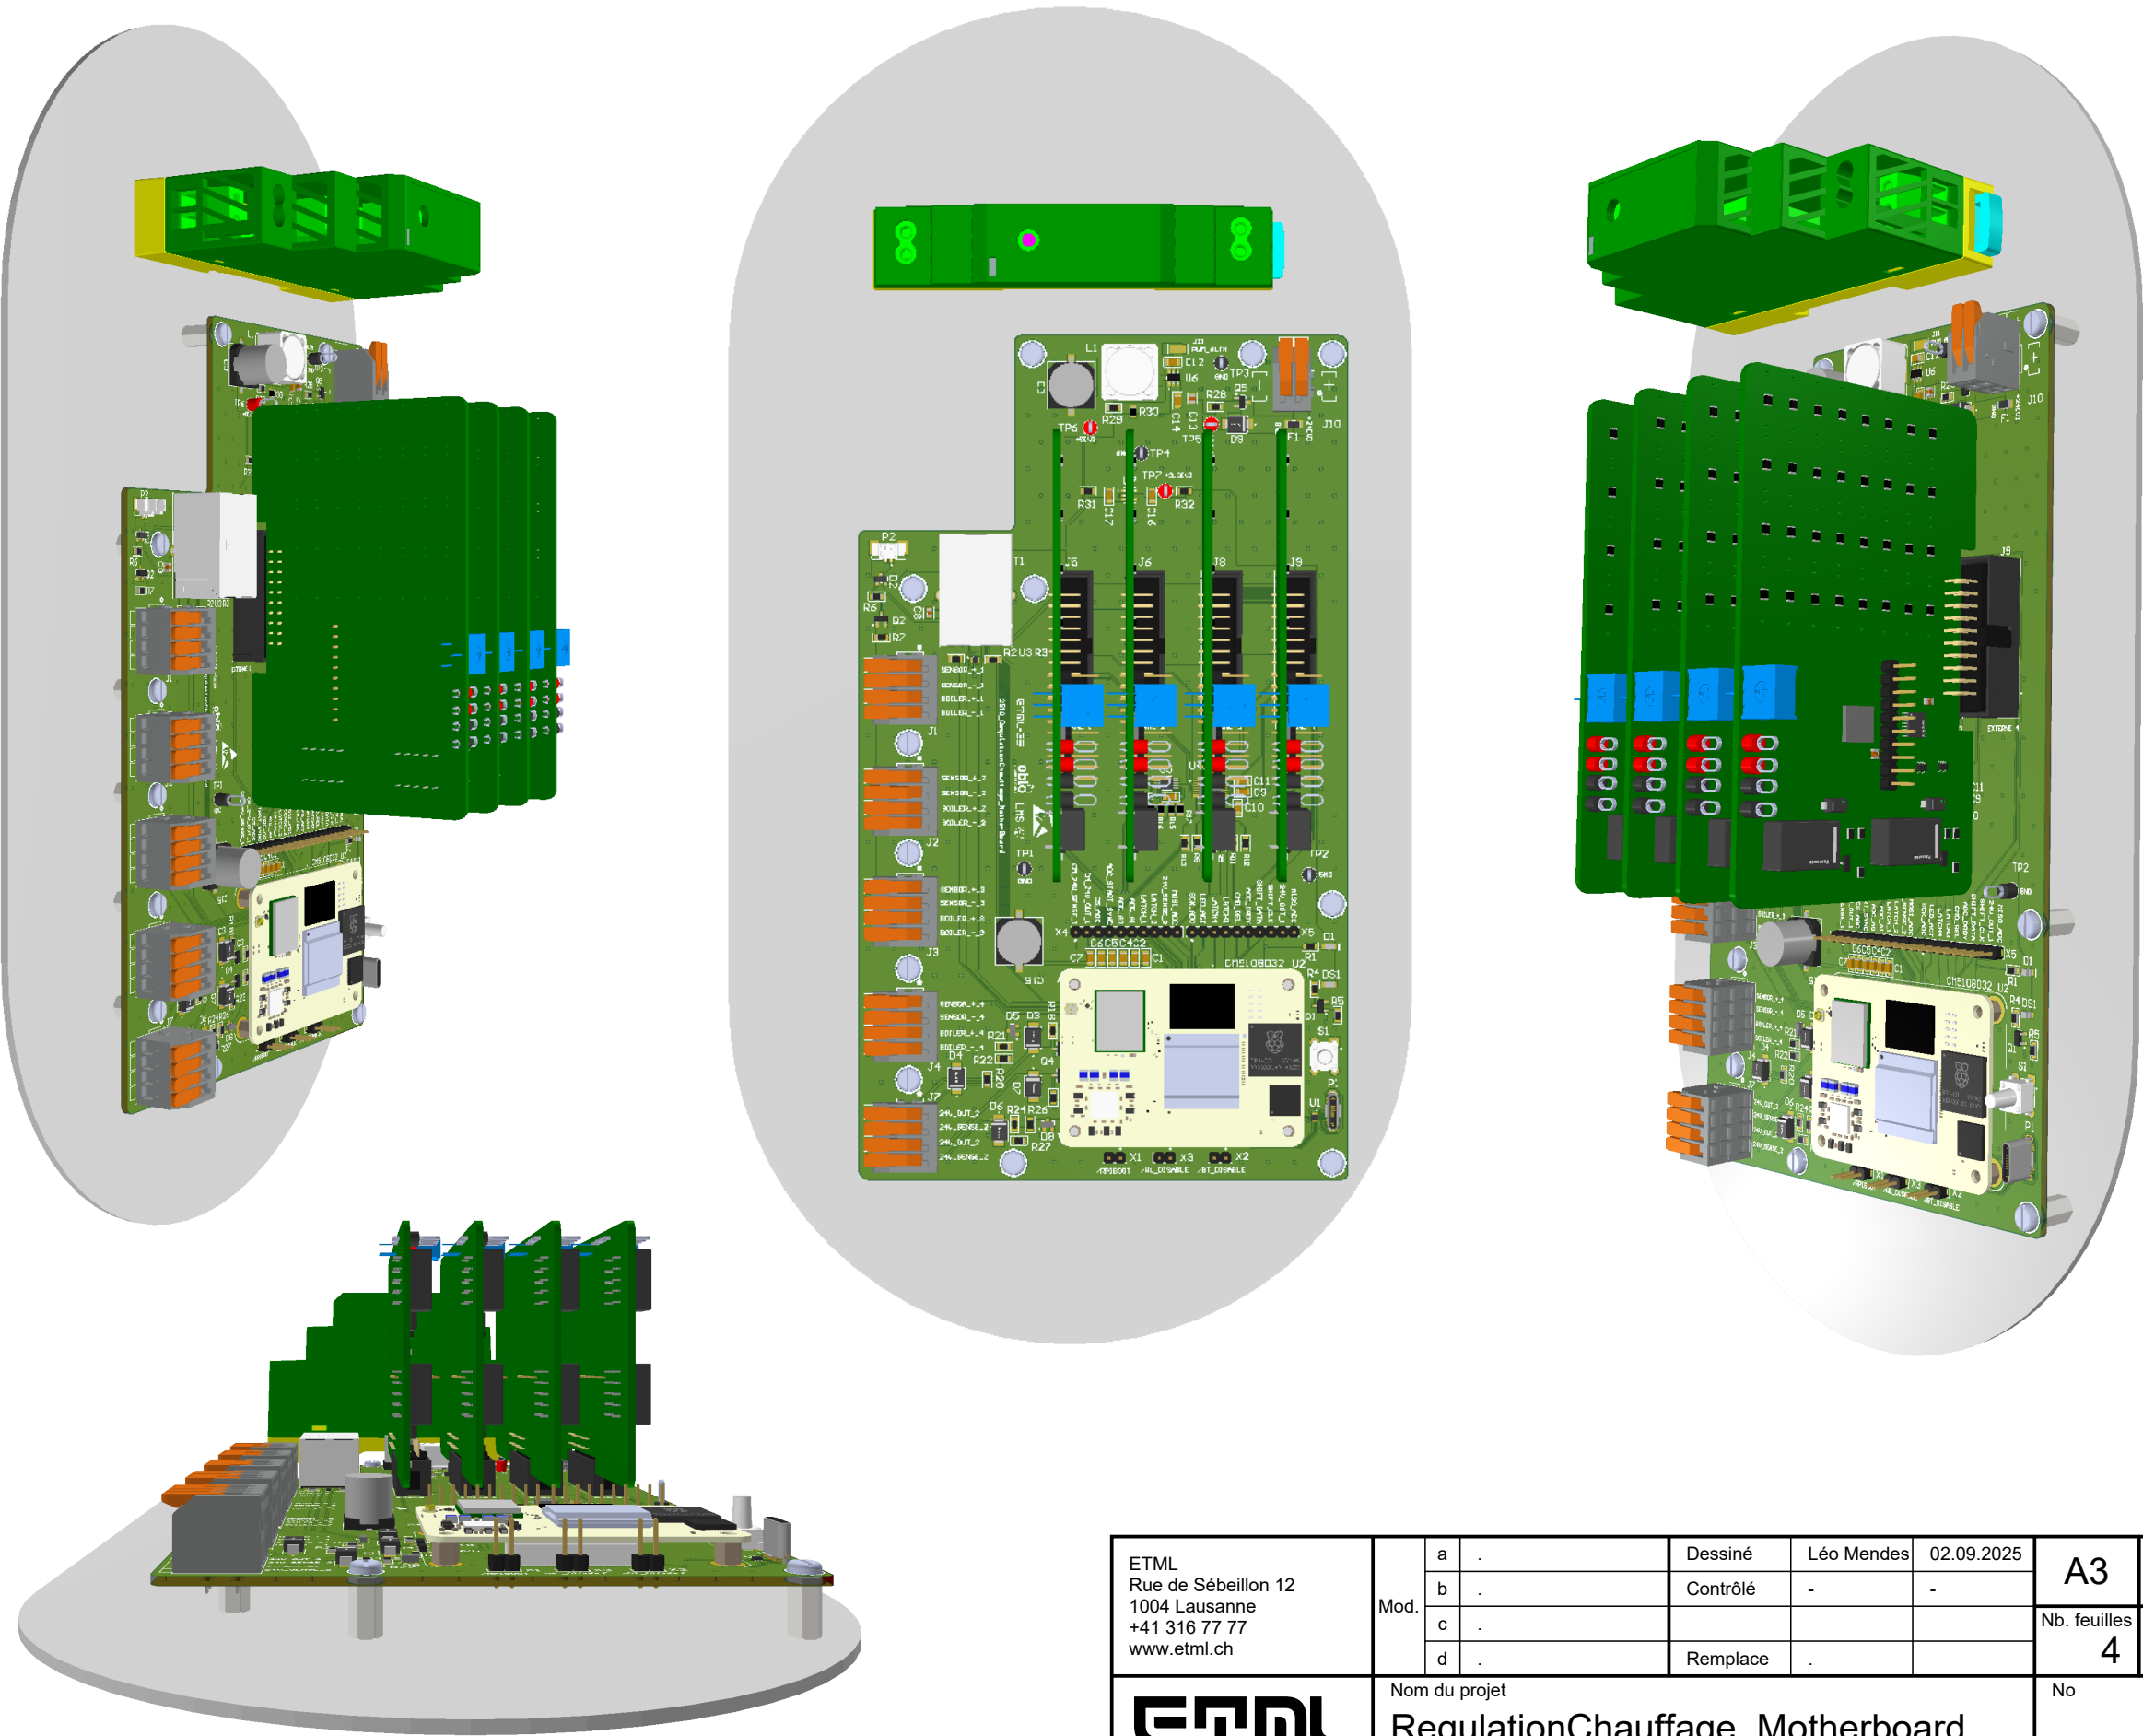

4

3

2

1

Mod.	a	.	Dessiné	Léo Mendes	02.09.2025	A3		Echelle : 2:1
	b	.	Contrôlé	-	-			
	c	.				Nb. feuilles	Feuille n°	
	d	.	Remplace	.		4	4	
ETML Rue de Sébeillon 12 1004 Lausanne +41 316 77 77 www.etml.ch			Nom du projet RegulationChauffage_Motherboard				No 2510	